
# RENO, APPARTEMENT DE DÉMONSTRATION

CANALISATIONS · implantation générale sur le plan courant

**MODÈLE 2 / 2026-10-12**

CONCEPTION · COTES À RELEVER

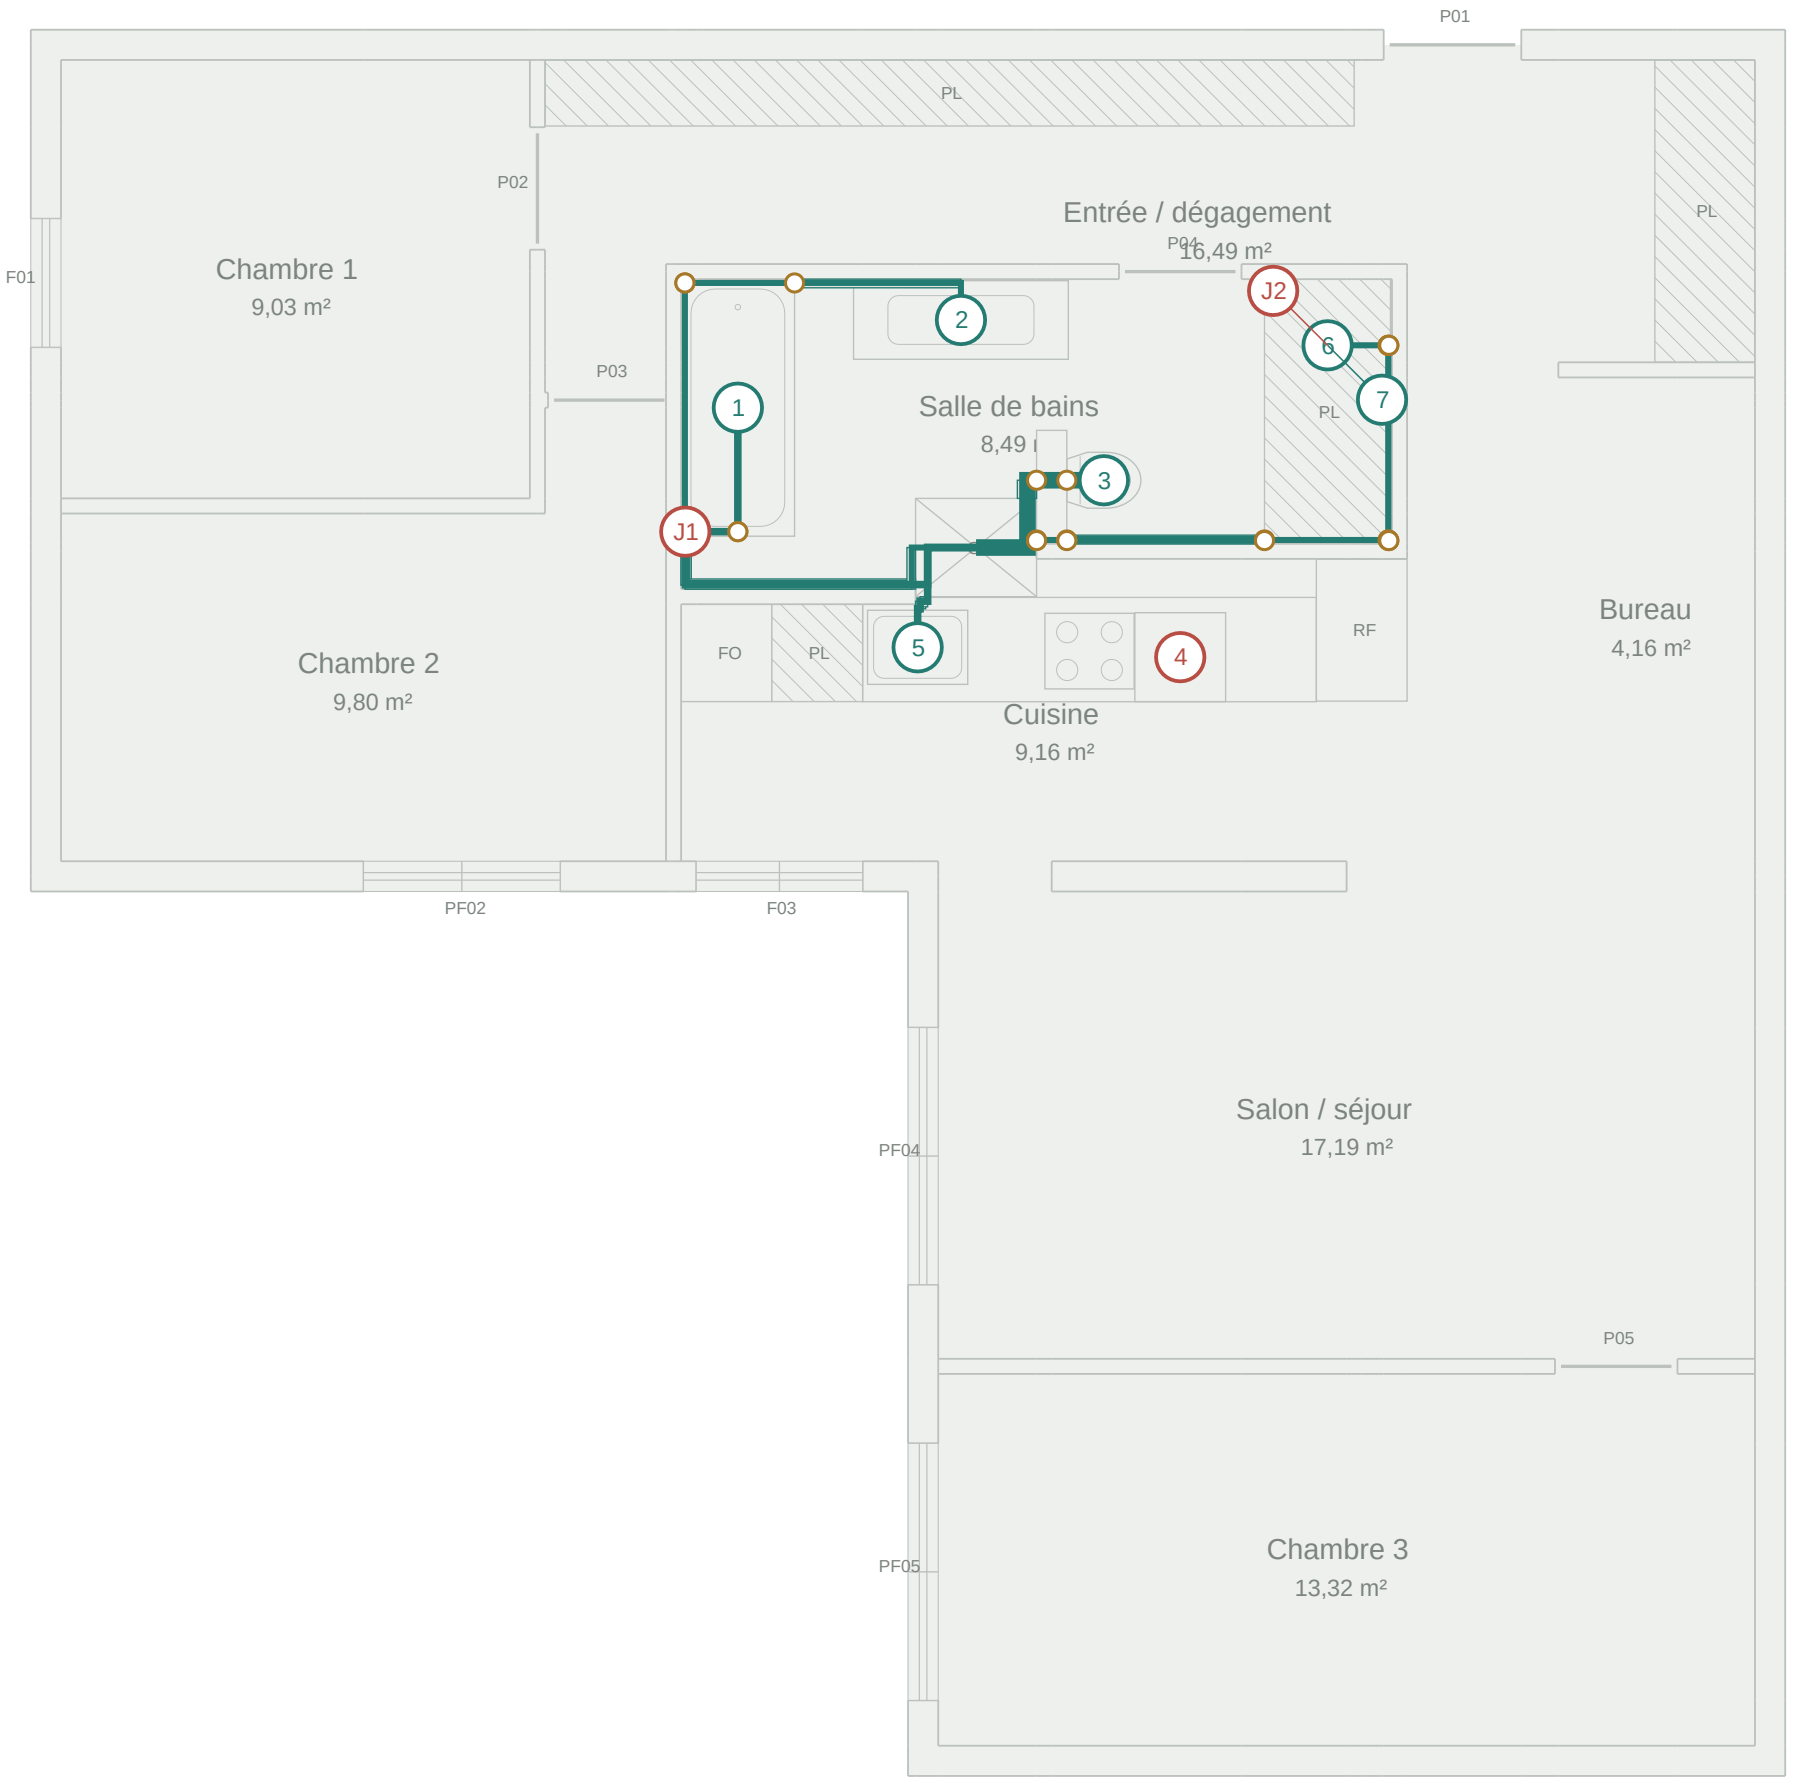


Branche compatible géométriquement

Parcours non admissible avec les réglages actuels

Traversée localisée à réserver / vérifier

**A3 · ÉCHELLE 1:50**

Impression à 100 %

6 branches compatibles sur 7 points recensés ; 2 rencontre(s) entre branches à résoudre. Les numéros relient le plan aux tableaux et profils. Les parcours refusés restent repérables mais ne produisent aucun coffrage en 3D.


Sol fini : 0,00. Implantations et altitudes issues du plan affiché. Ce dossier est une étude géométrique, pas un relevé des branchements existants ni un plan d'exécution validé.

# RENO, APPARTEMENT DE DÉMONSTRATION

CANALISATIONS · focus sur les cheminements

**MODÈLE 2 / 2026-10-12**

CONCEPTION · COTES À RELEVER

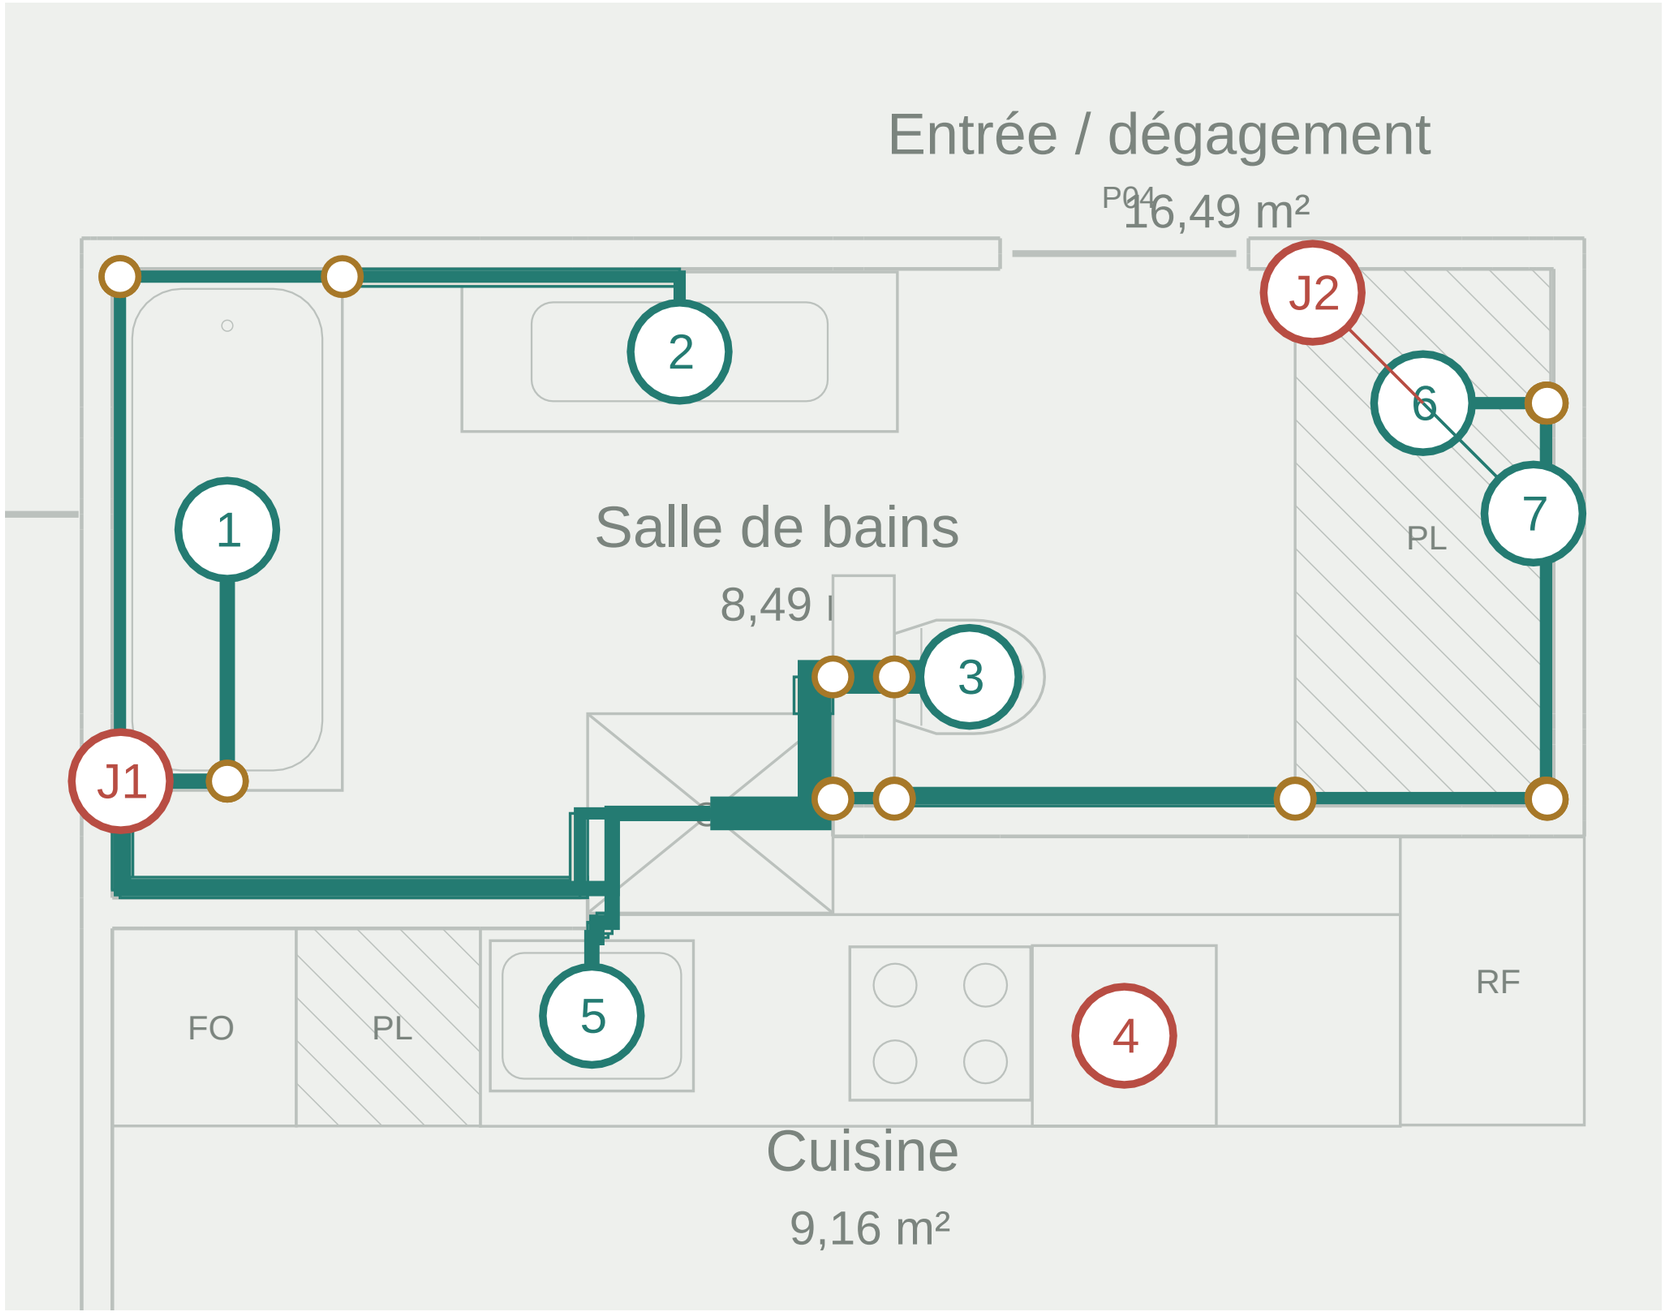


## REPÉRAGE DES BRANCHES

**1 · Baignoire**
Ø 50 mm · 3,68 m · 2 %

**2 · Plan vasque**
Ø 40 mm · 6,25 m · 2 %

**3 · Cuvette WC**
Ø 110 mm · 1,29 m · 6,2 %

**4 · Lave-vaisselle intégré**
Ø - mm · 0 m · À ADAPTER

**5 · Évier**
Ø 50 mm · 1,05 m · 7,65 %

**6 · Lave-linge**
Ø 40 mm · 4,46 m · 2 %

**7 · Sèche-linge**
Ø 32 mm · 4,47 m · 2 %

**Détail 1:20 · même origine et même géométrie que la vue générale.**


Tracés sur l'axe des tubes. Les traversées des cloisons légères et coffrages sont explicites ; les porteurs restent bloquants. Parcours contre les parois, sans raccourci au sol ni coffrage dans une circulation. PL : passage derrière, fond/plinthe à adapter. Aucun passage sous le sol fini.

# RENO, APPARTEMENT DE DÉMONSTRATION

COFFRAGES · repérage et cotes du plan courant

**MODÈLE 2 / 2026-10-12**

CONCEPTION · COTES À RELEVER

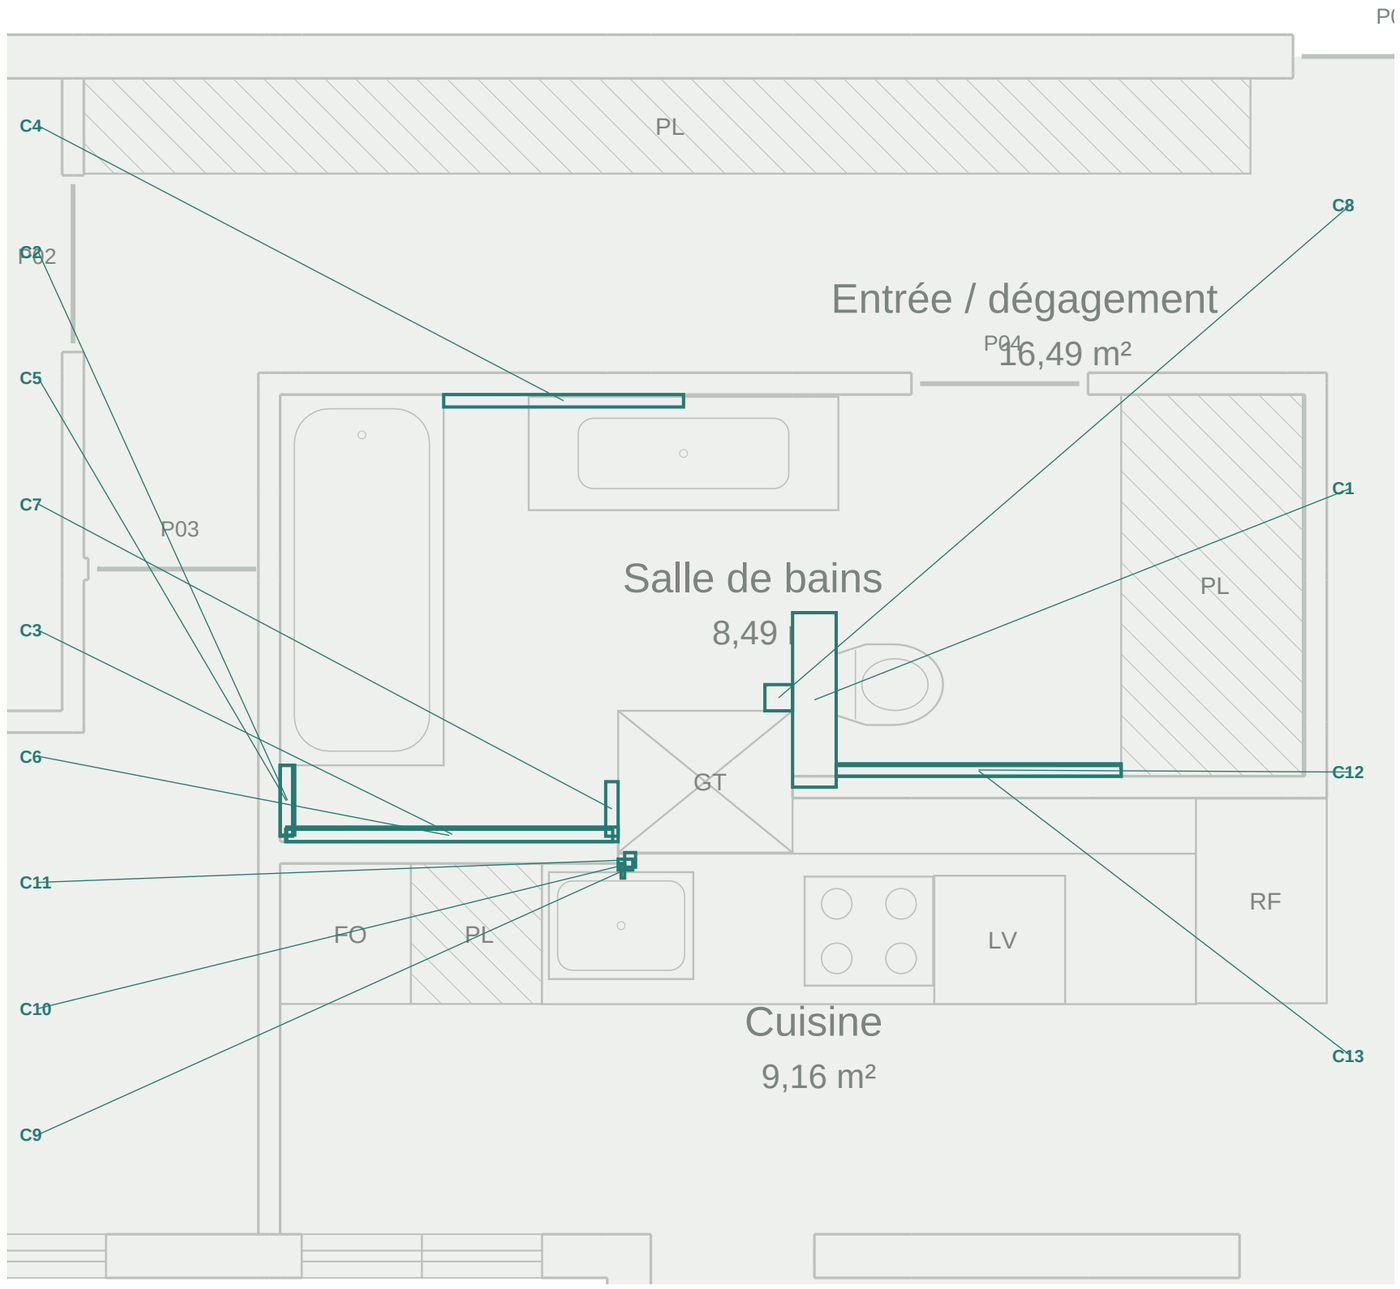


## COTES HORS TOUT · cm

Longueur × profondeur × hauteur

**C1 · Bâti WC**
80 × 20 × 118 · Existant / inclus

**C2 · Baignoire**
32 × 6,7 × 12,2 · Réseau calculé

**C3 · Baignoire**
152 × 6,7 × 11,6 · Réseau calculé

**C4 · Plan vasque**
110 × 5,7 × 17,7 · Réseau calculé

**C5 · Plan vasque**
32,5 × 5,7 × 10,7 · Réseau calculé

**C6 · Plan vasque**
150 × 5,7 × 10,1 · Réseau calculé

**C7 · Plan vasque**
25 × 5,7 × 7,1 · Réseau calculé

**C8 · Cuvette WC**
12,7 × 12 × 18,6 · Réseau calculé

**C9 · Évier**
6,7 × 1,6 × 16,8 · Réseau calculé

**C10 · Évier**
6,7 × 5 × 16,6 · Réseau calculé

**C11 · Évier**
6,7 × 5 × 16,2 · Réseau calculé

**C12 · Lave-linge**
130,7 × 5,7 × 13,2 · Réseau calculé

**C13 · Sèche-linge**
130,7 × 4,9 × 12,8 · Réseau calculé

Repères C reliés aux emprises réelles. Dimensions hors tout, hauteur depuis le bas physique du coffrage. Tablier et plage liés au rebord de baignoire ; coffrages du réseau issus des parcours. Accès, réservations et épaisseurs de construction à confirmer.

# RENO, APPARTEMENT DE DÉMONSTRATION

CANALISATIONS · nomenclature et vérifications

**MODÈLE 2 / 2026-10-12**

CONCEPTION · COTES À RELEVER

| N° | Point d'écoulement | Ø mm | L m | A cm | C cm | B cm | Pente % | Angle ° | Résultat |
|---|---|---|---|---|---|---|---|---|---|
| 1 | Baignoire | 50 | 3,68 | 12,4 | 10,9 | 3,5 | 2 | 1,15 | **Compatible *** |
| 2 | Plan vasque | 40 | 6,25 | 55 | 15 | 2,5 | 2 | 1,15 | **Compatible *** |
| 3 | Cuvette WC | 110 | 1,29 | 21 | 15 | 7 | 6,2 | 3,55 | **Compatible *** |
| 4 | Lave-vaisselle intégré | - | 0 | - | - | - | Pompé | - | **À adapter** |
| 5 | Évier | 50 | 1,05 | 55 | 15 | 7 | 7,65 | 4,37 | **Compatible *** |
| 6 | Lave-linge | 40 | 4,46 | 65 | 15 | 6,1 | 2 | 1,15 | **Compatible *** |
| 7 | Sèche-linge | 32 | 4,47 | 65 | 15 | 6,1 | 2 | 1,15 | **Compatible *** |

L : parcours horizontal développé, raccord appareil-paroi compris. A : axe de sortie après siphon / réception machine. C : départ du rampant après descente. B : axe à la colonne. Diamètres extérieurs de branches et diamètre de colonne : 110 mm.

* Compatible = géométrie de la branche seule avec ces hypothèses. Les rencontres J sont détaillées à la page suivante lorsqu'elles existent. Collecteurs communs, débits, ventilation, coudes, étanchéité, colliers et structure du support nécessitent une étude de pose. Pompé : longueur 3D du flexible relevé, sans pente gravitaire. Réception à l'évier puis une seule branche aval ; références et relevés détaillés dans le profil.

## J1 · Baignoire / Plan vasque

Rencontre entre Baignoire et Plan vasque : raccord commun ou décalage de pose à définir.

Repère du plan : x 4,23 m ; y 3,22 m · axe 8,1 cm au-dessus du sol fini.

## J2 · Lave-linge / Sèche-linge


Rencontre entre Lave-linge et Sèche-linge : raccord commun ou décalage de pose à définir.

Repère du plan : x 8,47 m ; y 1,99 m · axe 15 cm au-dessus du sol fini.

Un croisement de traits ne constitue pas un raccord dimensionné. Définir un collecteur commun, ses raccords et débits, ou une séparation physique respectant pente, sol et obstacles. Aucun raccord commun n'est validé automatiquement.

## 1 · Baignoire

Profil indicatif · axes vertical et horizontal à échelles distinctes

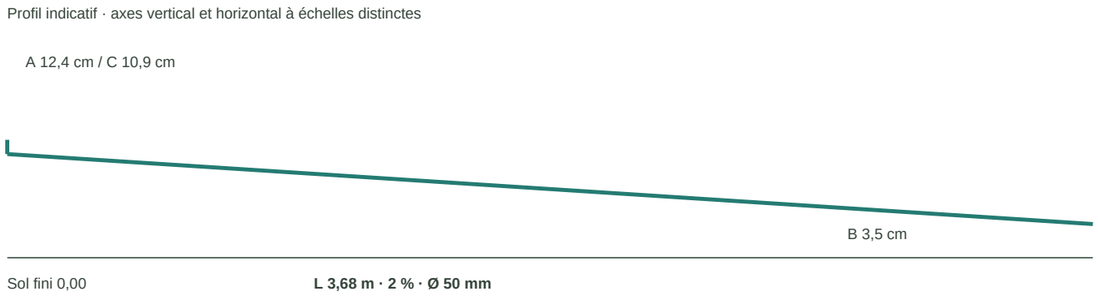


### BRANCHE COMPATIBLE

Pente, altitude et obstacles : compatibles pour cette branche.

Vide sous cuve et habillage existant : parcours libre dans cette emprise, sous contrôle de hauteur, sans coffrage ajouté. Hors baignoire, reprendre le mur.

Tube fixé au mur par colliers ; coffrage démontable uniquement contre les parois. PL traversé : fond/plinthe à adapter, sans coffrage dans la circulation. Entraxe selon fabricant.


Traversées : Baignoire. Destination : colonne dans la gaine du plan.

Encombrement du rampant : 139 mm au départ. Coffrage calculé : largeur 6,7 cm ; hauteur maximale 12,2 cm. À transmettre : point A selon le siphon réel ; cote B à relever ; réserve dans les fonds de meubles ; accès démontable aux raccords. Coffrage creux proposé : panneaux de 12 mm, rives reposant sur le sol, dessus démontable ; aucun dimensionnement mécanique des supports.

Équipement rehaussé de 39 mm ; support et raccords à adapter à cette cote. Descente courte : encombrement des raccords à vérifier. Point de sortie et raccord interne à confirmer selon le produit.

## 2 · Plan vasque

Profil indicatif · axes vertical et horizontal à échelles distinctes

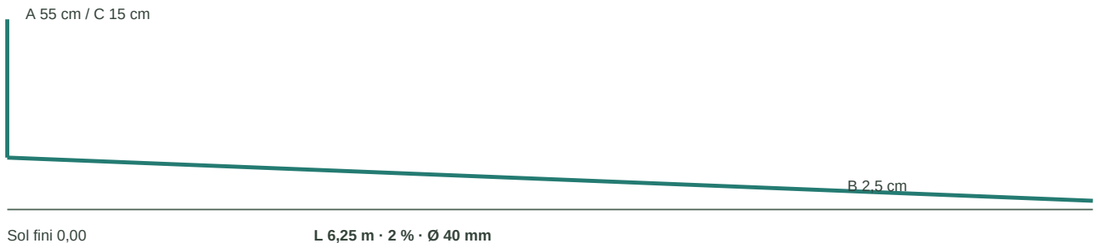


### BRANCHE COMPATIBLE

Pente, altitude et obstacles : compatibles pour cette branche.

Siphon et raccord intérieur de vasque ; rampant au ras du mur et du sol avec coffrage démontable. Le meuble vasque ne crée pas une cavité traversable.

Tube fixé au mur par colliers ; coffrage démontable uniquement contre les parois. PL traversé : fond/plinthe à adapter, sans coffrage dans la circulation. Entraxe selon fabricant.


Traversées : Baignoire. Destination : colonne dans la gaine du plan.

Encombrement du rampant : 175 mm au départ. Coffrage calculé : largeur 5,7 cm ; hauteur maximale 17,7 cm. À transmettre : point A selon le siphon réel ; cote B à relever ; réserve dans les fonds de meubles ; accès démontable aux raccords. Coffrage creux proposé : panneaux de 12 mm, rives reposant sur le sol, dessus démontable ; aucun dimensionnement mécanique des supports.

Point de sortie et raccord interne à confirmer selon le produit.

## 3 · Cuvette WC

Profil indicatif · axes vertical et horizontal à échelles distinctes

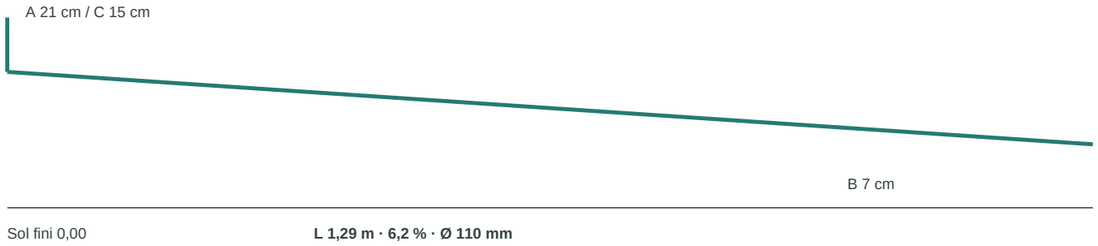


### BRANCHE COMPATIBLE

Pente, altitude et obstacles : compatibles pour cette branche.

Sortie de cuvette vers le bâti et la colonne ; contrôler diamètre et réservation. Le vide du bâti existant peut recevoir la branche.

Tube fixé au mur par colliers ; coffrage démontable uniquement contre les parois. PL traversé : fond/plinthe à adapter, sans coffrage dans la circulation. Entraxe selon fabricant.


Traversées : Bâti WC. Destination : colonne dans la gaine du plan.

Encombrement du rampant : 210 mm au départ. Coffrage calculé : largeur 12,7 cm ; hauteur maximale 18,6 cm. À transmettre : point A selon le siphon réel ; cote B à relever ; réserve dans les fonds de meubles ; accès démontable aux raccords. Coffrage creux proposé : panneaux de 12 mm, rives reposant sur le sol, dessus démontable ; aucun dimensionnement mécanique des supports.

Descente courte : encombrement des raccords à vérifier. Point de sortie et raccord interne à confirmer selon le produit.

## 5 · Évier

Profil indicatif · axes vertical et horizontal à échelles distinctes

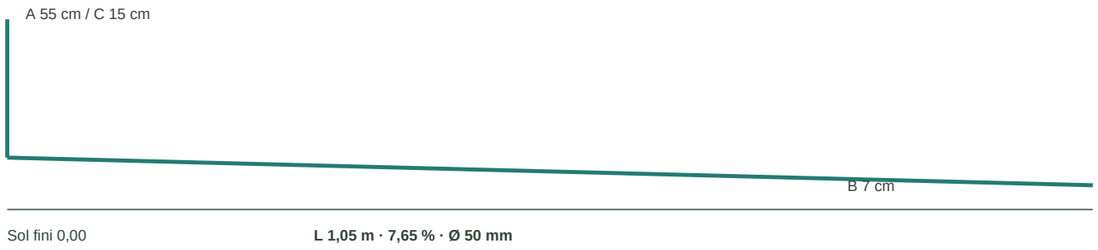


### BRANCHE COMPATIBLE

Pente, altitude et obstacles : compatibles pour cette branche.

Sortie après siphon ; rampant contre le mur dans un coffrage au sol. Le meuble sous évier ne permet aucun raccourci dans la pièce.

Tube fixé au mur par colliers ; coffrage démontable uniquement contre les parois. PL traversé : fond/plinthe à adapter, sans coffrage dans la circulation. Entraxe selon fabricant.


Traversées : aucune. Destination : colonne dans la gaine du plan.

Encombrement du rampant : 180 mm au départ. Coffrage calculé : largeur 6,7 cm ; hauteur maximale 16,8 cm. À transmettre : point A selon le siphon réel ; cote B à relever ; réserve dans les fonds de meubles ; accès démontable aux raccords. Coffrage creux proposé : panneaux de 12 mm, rives reposant sur le sol, dessus démontable ; aucun dimensionnement mécanique des supports.

Point de sortie et raccord interne à confirmer selon le produit.

## 6 · Lave-linge

Profil indicatif · axes vertical et horizontal à échelles distinctes

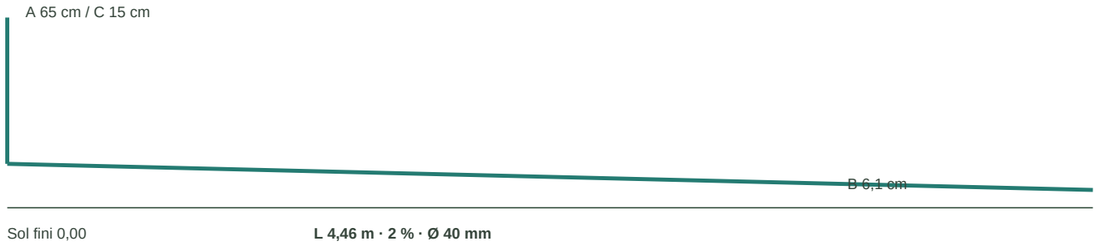


### BRANCHE COMPATIBLE

Pente, altitude et obstacles : compatibles pour cette branche.

Le flexible de machine rejoint un point A avec siphon selon sa notice. Ensuite, rampant coffré au mur et au sol ; réserve arrière du PL à adapter.

Tube fixé au mur par colliers ; coffrage démontable uniquement contre les parois. PL traversé : fond/plinthe à adapter, sans coffrage dans la circulation. Entraxe selon fabricant.


Traversées : Placard buanderie ; Bâti WC. Destination : colonne dans la gaine du plan.

Encombrement du rampant : 175 mm au départ. Coffrage calculé : largeur 5,7 cm ; hauteur maximale 13,2 cm. À transmettre : point A selon le siphon réel ; cote B à relever ; réserve dans les fonds de meubles ; accès démontable aux raccords. Coffrage creux proposé : panneaux de 12 mm, rives reposant sur le sol, dessus démontable ; aucun dimensionnement mécanique des supports.

PL à adapter : Placard buanderie ; réserver le passage derrière le meuble contre le mur et garder les raccords accessibles. Point de sortie et raccord interne à confirmer selon le produit.

## 7 · Sèche-linge

Profil indicatif · axes vertical et horizontal à échelles distinctes

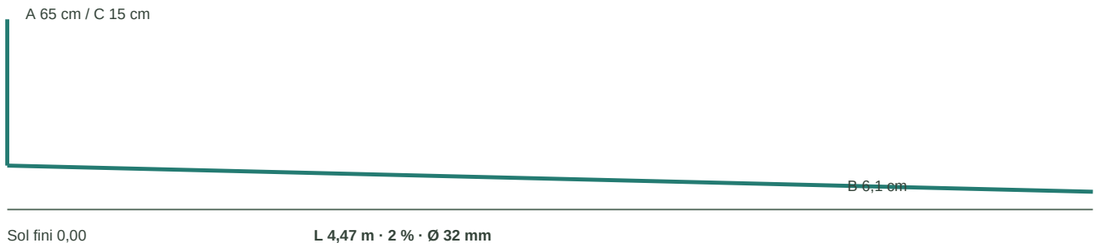


### BRANCHE COMPATIBLE

Pente, altitude et obstacles : compatibles pour cette branche.

Condensats seulement si appareil raccordable. Après réception A, rampant coffré contre le mur et le sol ; aucune traversée libre sous la machine.

Tube fixé au mur par colliers ; coffrage démontable uniquement contre les parois. PL traversé : fond/plinthe à adapter, sans coffrage dans la circulation. Entraxe selon fabricant.

Traversées : Placard buanderie ; Bâti WC. Destination : colonne dans la gaine du plan.

Encombrement du rampant : 171 mm au départ. Coffrage calculé : largeur 4,9 cm ; hauteur maximale 12,8 cm. À transmettre : point A selon le siphon réel ; cote B à relever ; réserve dans les fonds de meubles ; accès démontable aux raccords. Coffrage creux proposé : panneaux de 12 mm, rives reposant sur le sol, dessus démontable ; aucun dimensionnement mécanique des supports.

PL à adapter : Placard buanderie ; réserver le passage derrière le meuble contre le mur et garder les raccords accessibles. Point de sortie et raccord interne à confirmer selon le produit.

## 4 · Lave-vaisselle intégré > Récepteur absent

Raccord à définir ou à adapter.

Machine déclarée : référence inconnue. Siphon déclaré : référence inconnue.

Sortie machine : à relever. Réception siphon : à relever.

Flexible : Ø à relever mm ; longueur utile déclarée - m ; trajet 3D calculé non établi.

Évier récepteur absent : choisissez le poste réellement posé.

Référence du lave-vaisselle et notice de raccordement à identifier.

Siphon avec embout machine réellement posé à identifier.

Relevé des raccords à valider.

Sortie de machine : point 3D à relever.

Embout de siphon : point 3D à relever.

Longueur utile du flexible à relever.

Diamètre extérieur réel du flexible à relever.

Embout machine disponible et accessible à confirmer.

Compatibilité des embouts, collier et étanchéité à confirmer.

Flexible pompé jusqu'à l'embout déclaré du siphon ; la branche gravitaire de l'évier reprend ensuite l'écoulement. Aucun rampant ni rehausse de la machine.

Flexible maintenu contre la paroi, sans pincement ; embouts accessibles, collier et montage selon les notices. Aucun coffrage gravitaire supplémentaire.

Longueur utile déclarée ; la cote fabricant est approximative. Aucun raccord, débit simultané ou rayon de cintrage certifié par ce calcul.

Sources des limites proposées : notice IKEA LAGAN306.273.64, AA-2643461-2-1 p.5 (réception 40-80 cm, flexible environ 150 cm) ; fiche LILLVIKEN103.115.39. Une référence documentaire ne prouve pas le montage installé. Réservations non représentées : à relever avant validation.