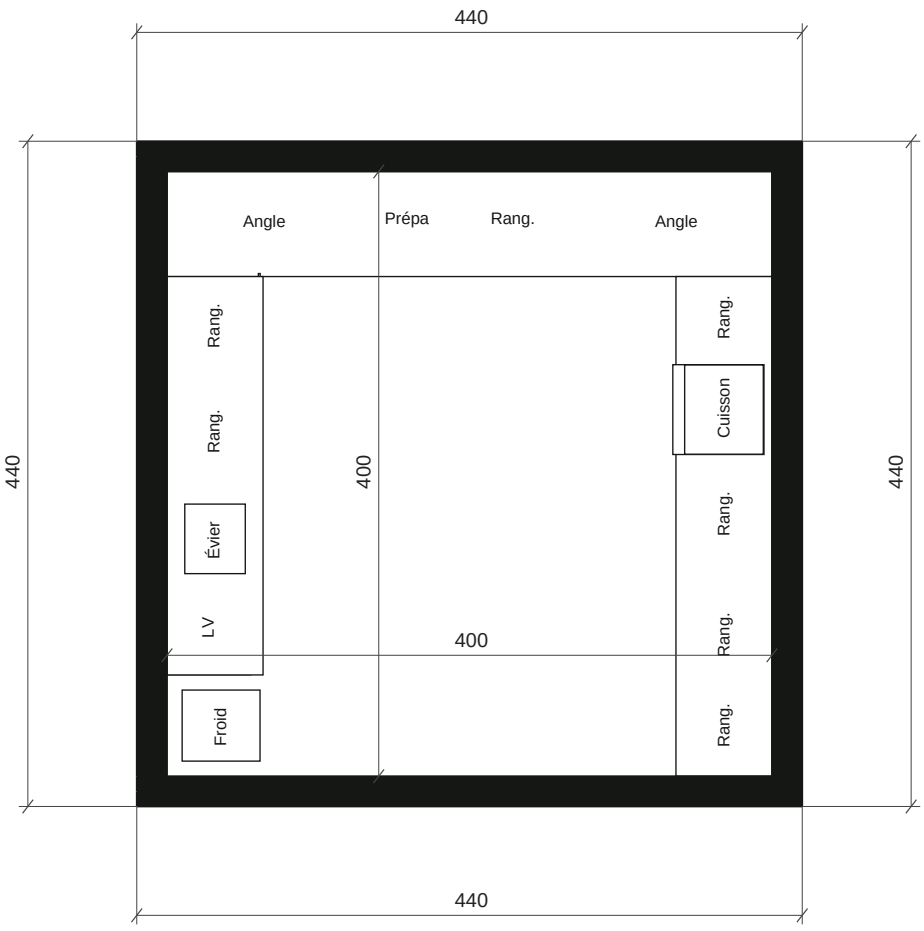

COTES DES ESPACES BÂTIS

Cotes entre faces des murs et cloisons. Les limites virtuelles des volumes ne coupent aucune longueur. Façades : chaînes des baies et retours, puis cotes totales.

SURFACE GÉOMÉTRIQUE

Intérieur des façades	**16,00 m²**

Pays du logement à renseigner. Sans certification Carrez.

ÉCHELLE 1:50

A3 · imprimer à 100 %

0 1 2 m

Épaisseurs du modèle : façades 20 cm

Murs foncés : porteurs / enveloppe · PL : placard · GT : gaine · P / F / PF : ouvrants
LV : lave-vaisselle · Prépa : préparation · Rang. : rangement.

Cotes en cm · HSP 250 cm · maquette de conception, sans visa d'exécution.

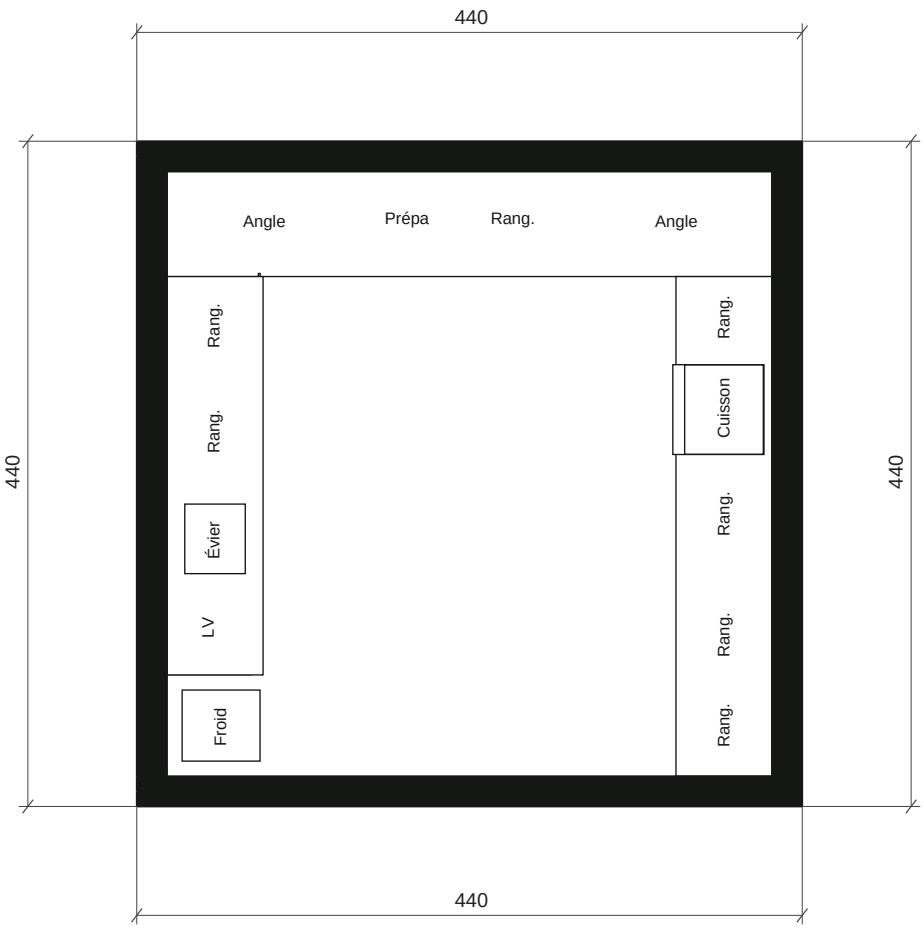

VOLUMES ET INTENTIONS

Limites virtuelles en tirets verts. Cotes des volumes souhaités, même sans cloison. Les m² par zone correspondent au sol disponible, seuils compris.

SURFACE GÉOMÉTRIQUE

Intérieur des façades	**16,00 m²**

Pays du logement à renseigner. Sans certification Carrez.

ÉCHELLE 1:50

A3 · imprimer à 100 %

0 1 2 m

Épaisseurs du modèle : façades 20 cm

Murs foncés : porteurs / enveloppe · PL : placard · GT : gaine · P / F / PF : ouvrants
LV : lave-vaisselle · Prépa : préparation · Rang. : rangement.

OUVERTURES DU MODÈLE
STRUCTURE ET ÉQUIPEMENTS

reno-envelope-north · 420 × 250 × 20 cm
reno-envelope-east · 420 × 250 × 20 cm
reno-envelope-south · 420 × 250 × 20 cm
reno-envelope-west · 420 × 250 × 20 cm

ÉQUIPEMENTS FIXES REPRÉSENTÉS

METOD ASKERSUND · angle 128 · 127,5 × 67,5 cm
METOD/MAXIMERA ASKERSUND · 60 · 60 × 60,6 cm
METOD/MAXIMERA ASKERSUND · 80 · 80 × 60,6 cm
METOD ASKERSUND · angle 128 · 127,5 × 67,5 cm
LAGAN · froid pose libre · 51,5 × 47 cm
LAGAN · lave-vaisselle · 55,5 × 59,8 cm
METOD ASKERSUND · sous-évier 60 · 60,6 × 60 cm
METOD/MAXIMERA ASKERSUND · 80 · 60,6 × 80 cm
METOD/MAXIMERA ASKERSUND · 60 · 60,6 × 60 cm
METOD/MAXIMERA ASKERSUND · 60 · 60,6 × 60 cm
METOD/MAXIMERA ASKERSUND · four 60 · 60,6 × 60 cm
METOD/MAXIMERA ASKERSUND · 80 · 60,6 × 80 cm
METOD/MAXIMERA ASKERSUND · 80 · 60,6 × 80 cm
METOD/MAXIMERA ASKERSUND · 40 · 60,6 × 40 cm
Plan de travail · 5 × 1,2 cm
Plan de travail · 400 × 69,5 cm
Plan de travail · 1,2 × 5,5 cm
Plan de travail · 63,5 × 263,5 cm
Plan de travail · 1,2 × 12,5 cm
Plan de travail · 63,5 × 330,5 cm
LAGAN · four · 60,3 × 59,4 cm
VILSTA · induction · 52 × 59 cm
FYNDIG + LILLVIKEN · évier · 40 × 46 cm

Murs : longueurs d'axes. Cotes intérieures : entre faces du modèle. Vantail, réservation et passage utile sont distincts ; passage utile à confirmer par notice et relevé.

Base géométrique

Instantané du projet courant : PLAN, ARCHI, Visite et cet export utilisent la même géométrie. Les cotes sont celles du modèle ; un relevé sur place et sa provenance restent nécessaires avant travaux. Aucun dossier antérieur ne constitue une mesure du projet modifié.

Murs et structure

Épaisseurs indiquées dans la nomenclature : valeurs du modèle. Matériaux, doublages et caractère porteur à diagnostiquer avant intervention. L'époque de construction seule ne prouve ni composition ni capacité portante. Les modifications et études nécessaires doivent être documentées.

Hauteurs et repérage

Hauteur sous plafond du modèle : 250 cm. Sol fini local de référence 0,00 ; altitude géographique non renseignée. Nord, épaisseur des dalles et retombées restent à relever. Aucun étage supplémentaire ou repère géographique n'est déduit du dessin.

Portes

Les dimensions, mécanismes et réservations courants figurent dans la nomenclature. Vantail, passage utile et réservation sont des mesures distinctes. Les références commerciales conservent leurs dimensions fabricant ; un ouvrage adapté ou sur mesure doit rester identifié séparément. Huisseries et jeux de pose à vérifier.

Menuiseries et débattements

Positions, dimensions et allèges des fenêtres sont celles du modèle, à mesurer. Débattements et refoulements de portes suivent le mécanisme et le sens choisis dans Configuration ; le PDF utilise leur position conventionnelle ouverte, sans modifier leur état dans la visite. Les fenêtres suivent les mécanismes de la maquette ; sens, ferrures et menuiseries réelles restent à relever.

Gaine et réseaux

Aucune gaine active identifiée dans le modèle. Contenu, raccordements, altitudes, propriété et possibilités de modification restent à relever. Les canalisations sont recalculées depuis le même plan ; le dessin ne constitue pas une autorisation de déplacer une colonne collective.

Surfaces

Mesure géométrique au nu intérieur des façades. Murs intérieurs, cloisons et gaine inclus ; aucun seuil de hauteur ni abattement réglementaire. Ce nombre ne constitue ni une surface habitable ni une surface de plancher réglementaire. Hypothèse du calcul : logement clos sur un seul niveau, hauteur uniforme, sans annexe ni escalier représenté. Relevé et applicabilité au projet à confirmer.

Contexte des surfaces

Pays du logement à renseigner. Sans certification Carrez. Aucune déduction réglementaire appliquée à la mesure géométrique.

Présentation

Deux plans vectoriels A3 portrait : espaces bâtis d'abord, volumes souhaités ensuite. Nomenclature et méthode en A3 paysage. Même échelle pour les deux plans, impression à 100 %. Cotes entre faces du modèle ; baies cotées en réservation, distincte du vantail. Finitions et cotes de gros oeuvre à relever. Les réservations existantes sont conservées même si une jonction empiète dessus : aucune correction du projet par le dessin.

PORTÉE DU DOSSIER

Surfaces géométriques : aucun mesurage réglementaire local certifié.

Relevé, diagnostics, autorisations et études de structure ne sont pas produits par cet export.

Les pièces de dépôt administratif et les plans d'exécution dépendent du projet et de son territoire.