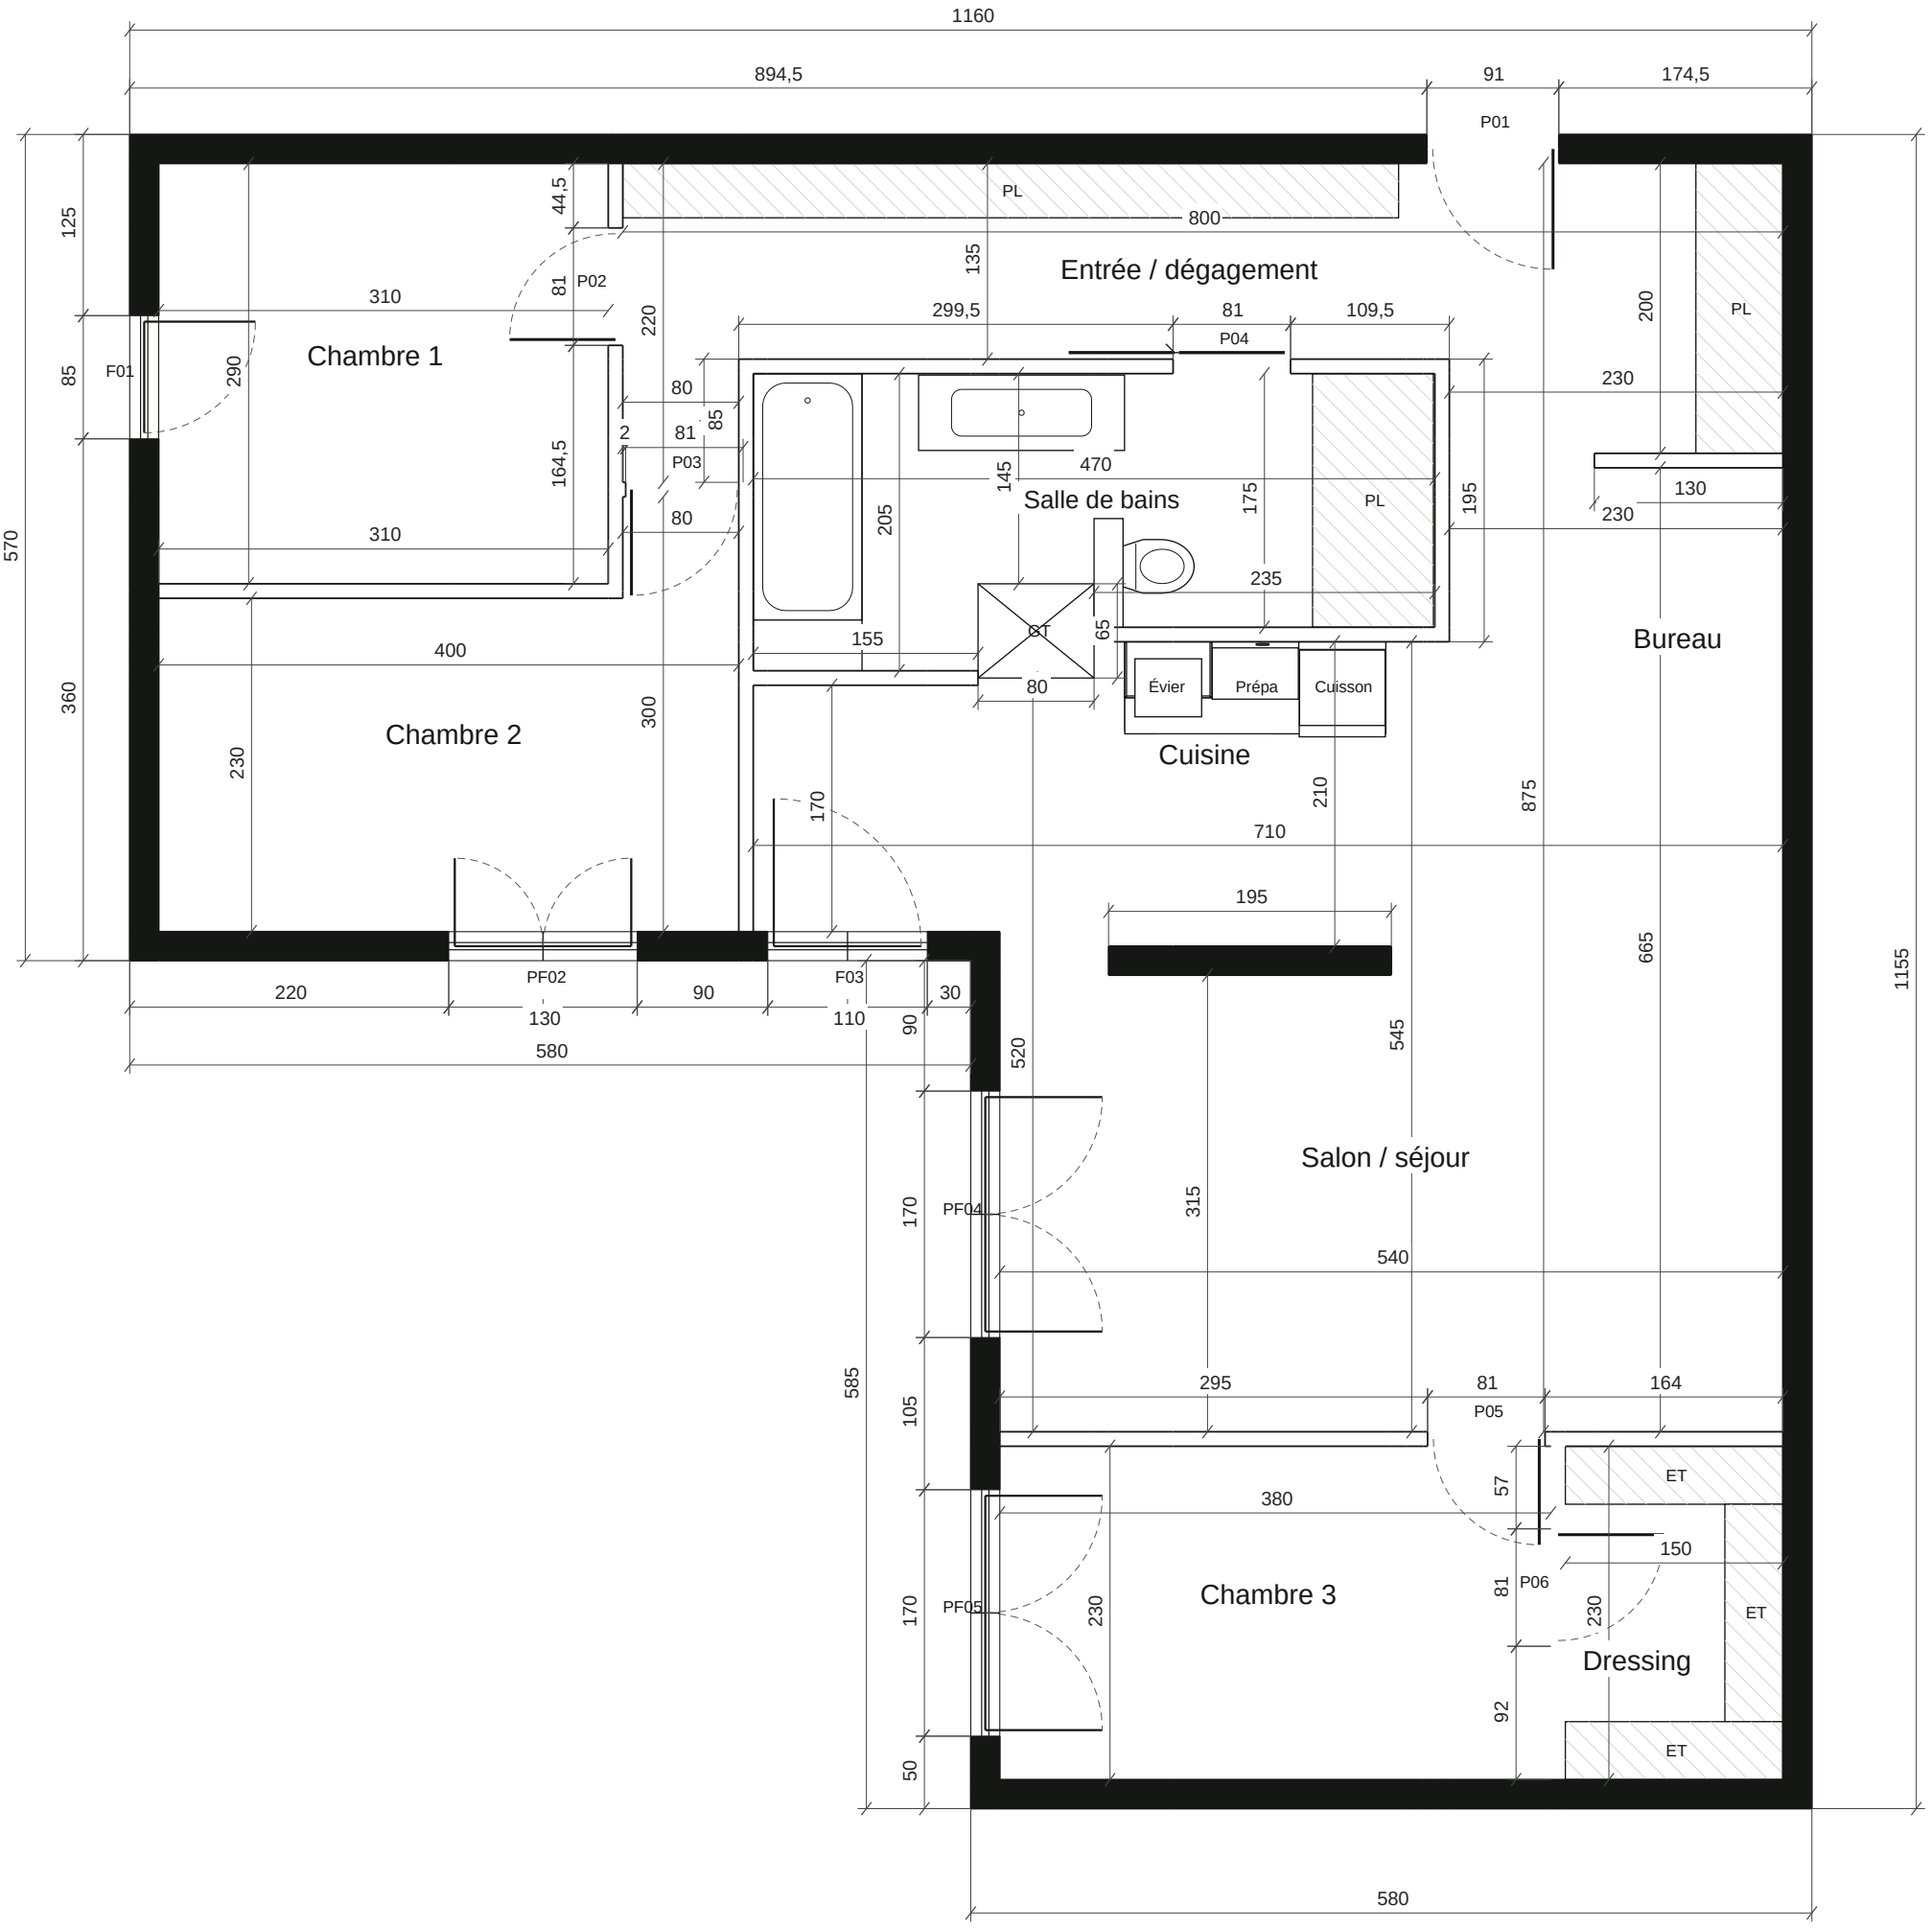


COTES DES ESPACES BÂTIS

Cotes entre faces des murs et cloisons. Les limites virtuelles des volumes ne coupent aucune longueur. Façades : chaînes des baies et retours, puis cotes totales.

SURFACE GÉOMÉTRIQUE

Intérieur des façades	**90,95 m²**

Pays du logement à renseigner. Sans certification Carrez.

ÉCHELLE 1:50


A3 · imprimer à 100 %

0 1 2 m

Épaisseurs du modèle : façades 20 cm · cloisons 10 cm · porteurs intérieurs 20 cm

Murs foncés : porteurs / enveloppe · PL : placard · GT : gaine · P / F / PF : ouvrants
LV : lave-vaisselle · Prépa : préparation · Rang. : rangement.

Cotes en cm · HSP 250 cm · maquette de conception, sans visa d'exécution.

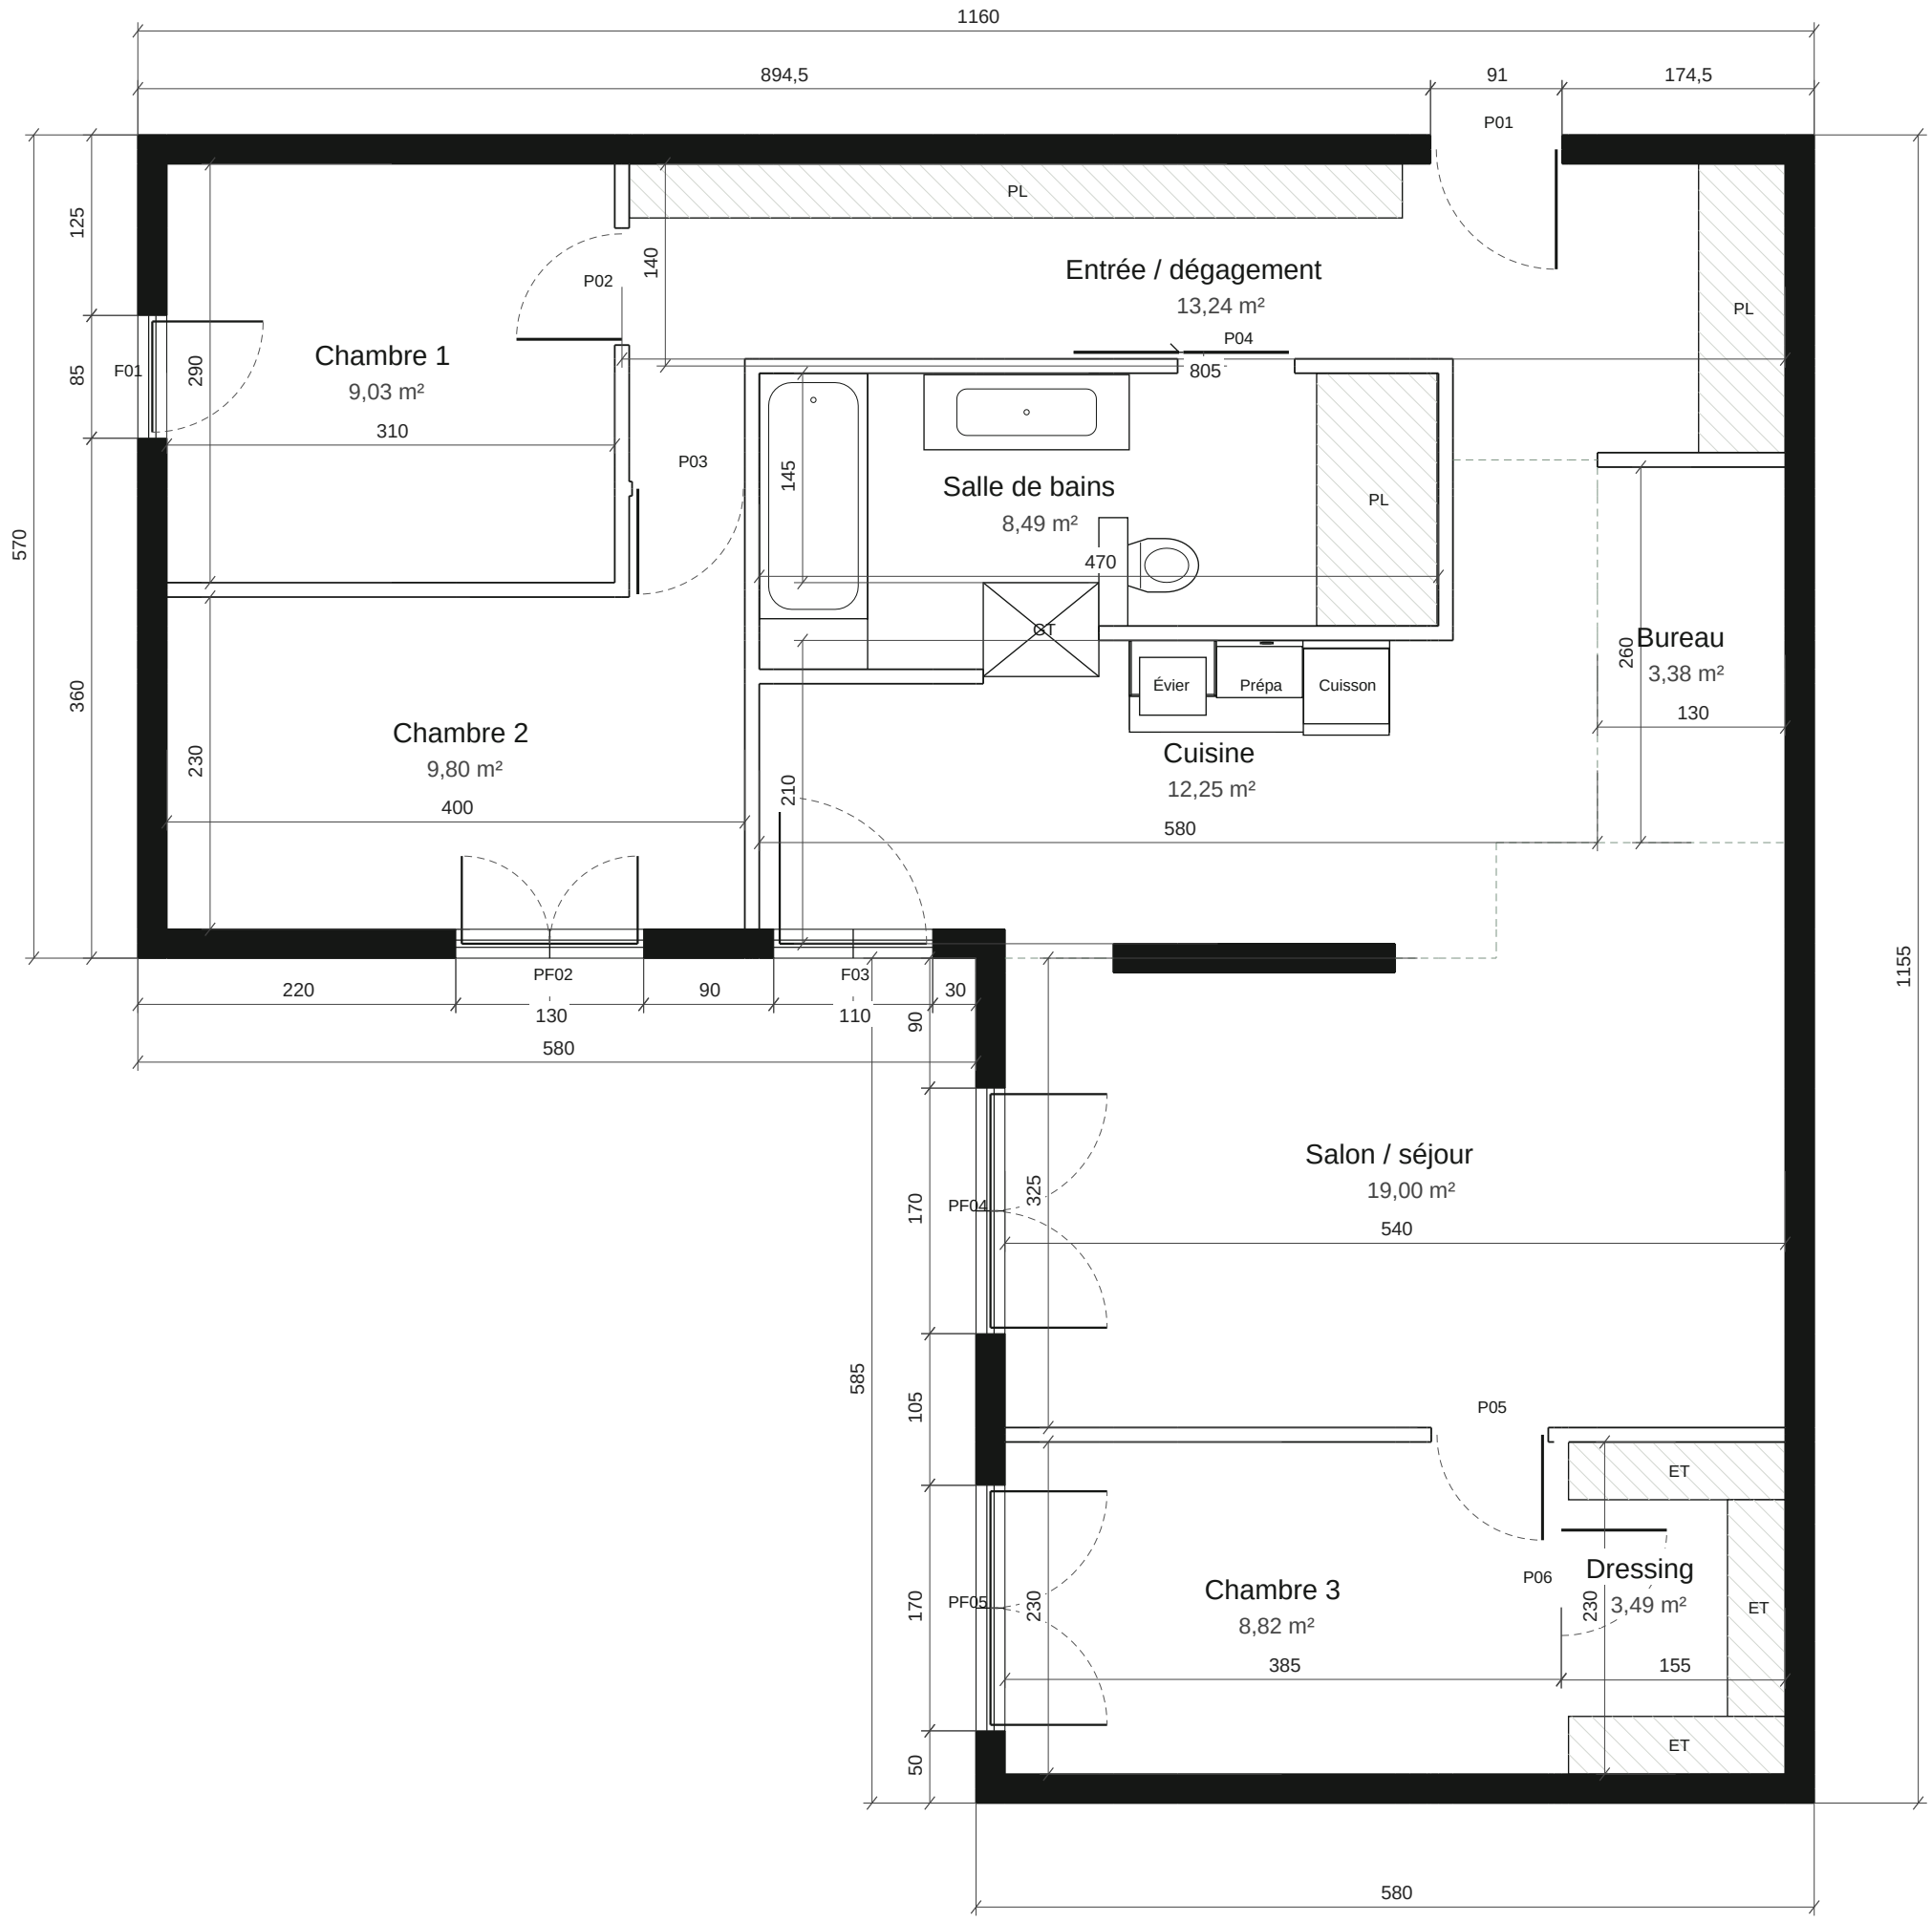

VOLUMES ET INTENTIONS

Limites virtuelles en tirets verts. Cotes des volumes souhaités, même sans cloison. Les m² par zone correspondent au sol disponible, seuils compris.

SURFACE GÉOMÉTRIQUE

Intérieur des façades	**90,95 m²**

Pays du logement à renseigner. Sans certification Carrez.

ÉCHELLE 1:50

A3 · imprimer à 100 %

0 1 2 m

Épaisseurs du modèle : façades 20 cm · cloisons 10 cm · porteurs intérieurs 20 cm

Murs foncés : porteurs / enveloppe · PL : placard · GT : gaine · P / F / PF : ouvrants
LV : lave-vaisselle · Prépa : préparation · Rang. : rangement.

Cotes en cm · HSP 250 cm · maquette de conception, sans visa d'exécution.